



天水常记呱呱餐饮管理有限责任公司用地范围图

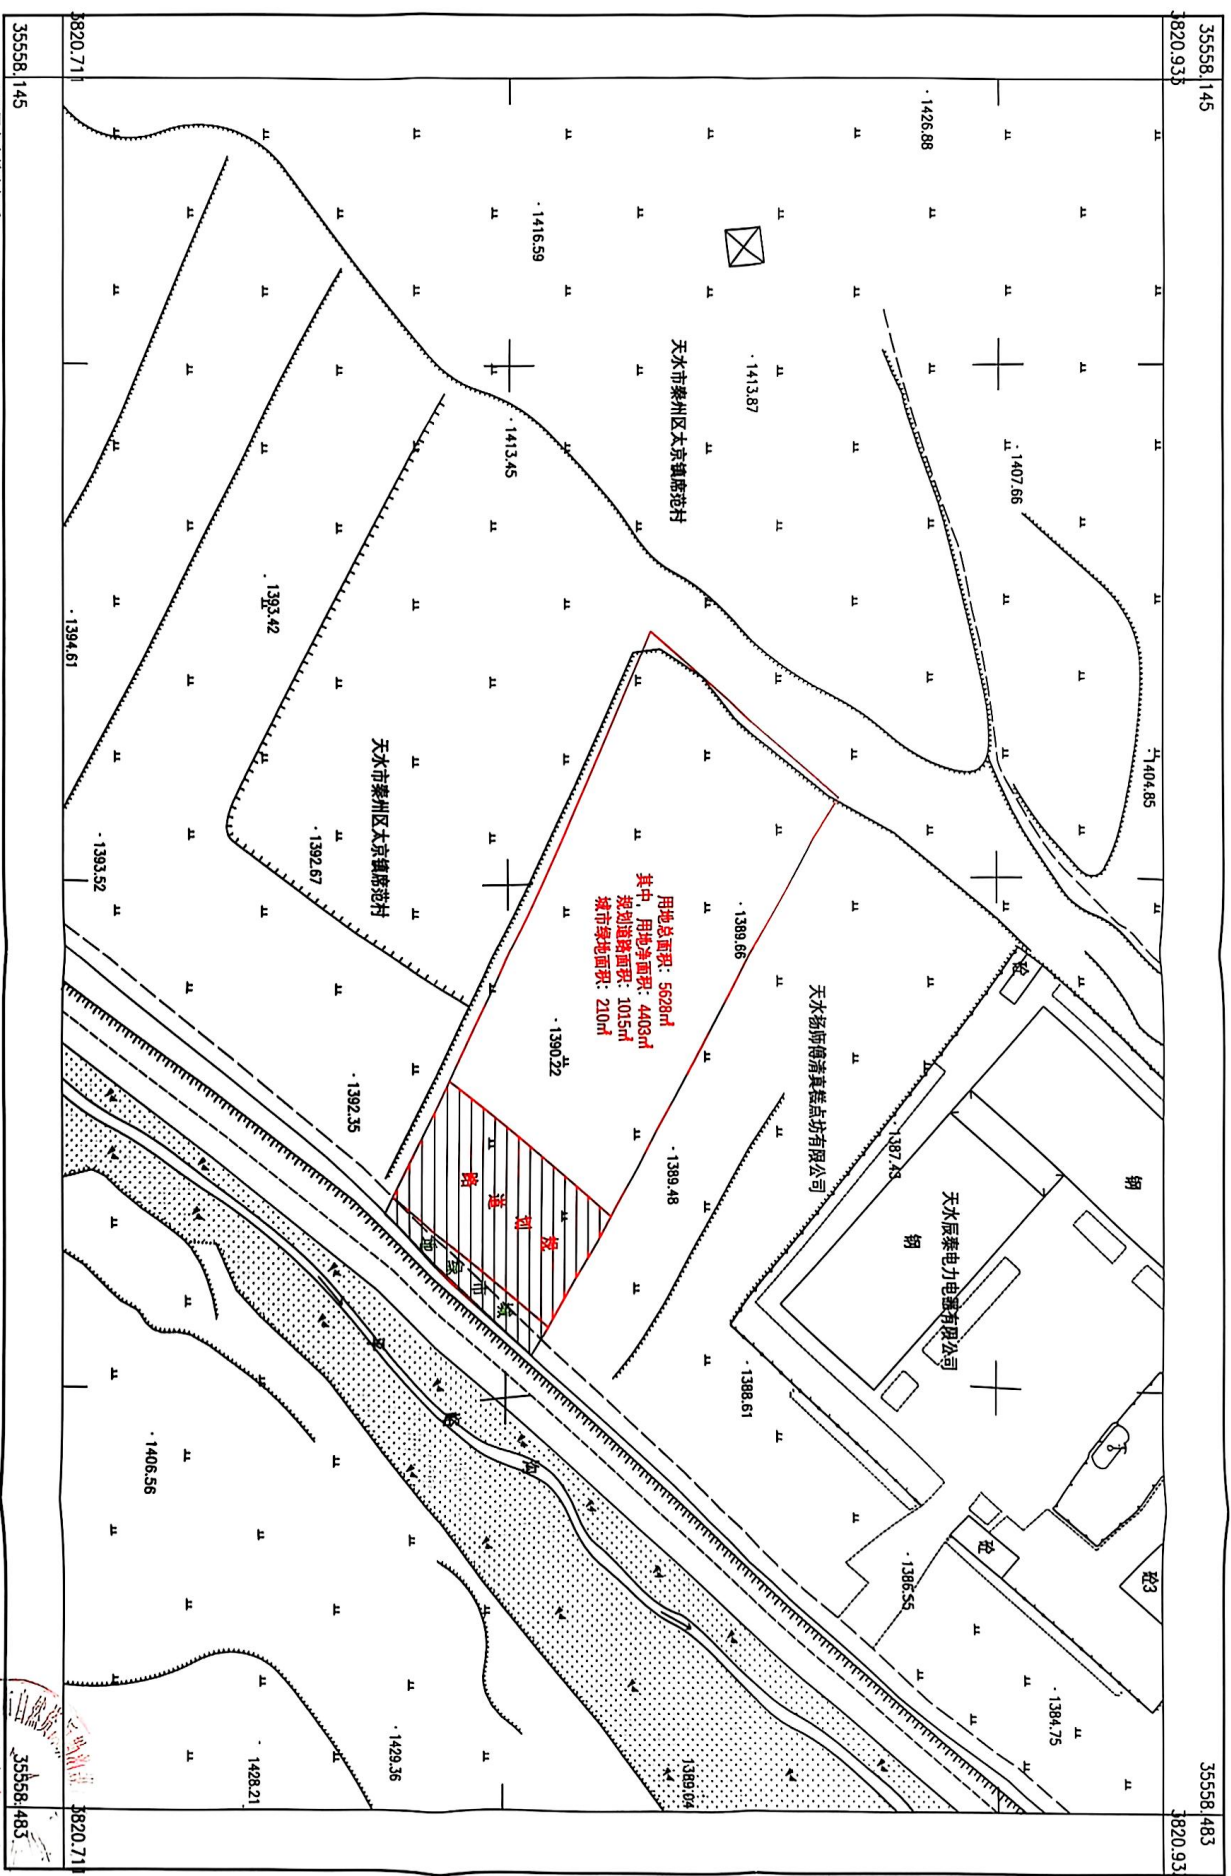

2000国家大地坐标系
1985国家高程基准
2017年版图式
2025年9月数字化成图

1:1000



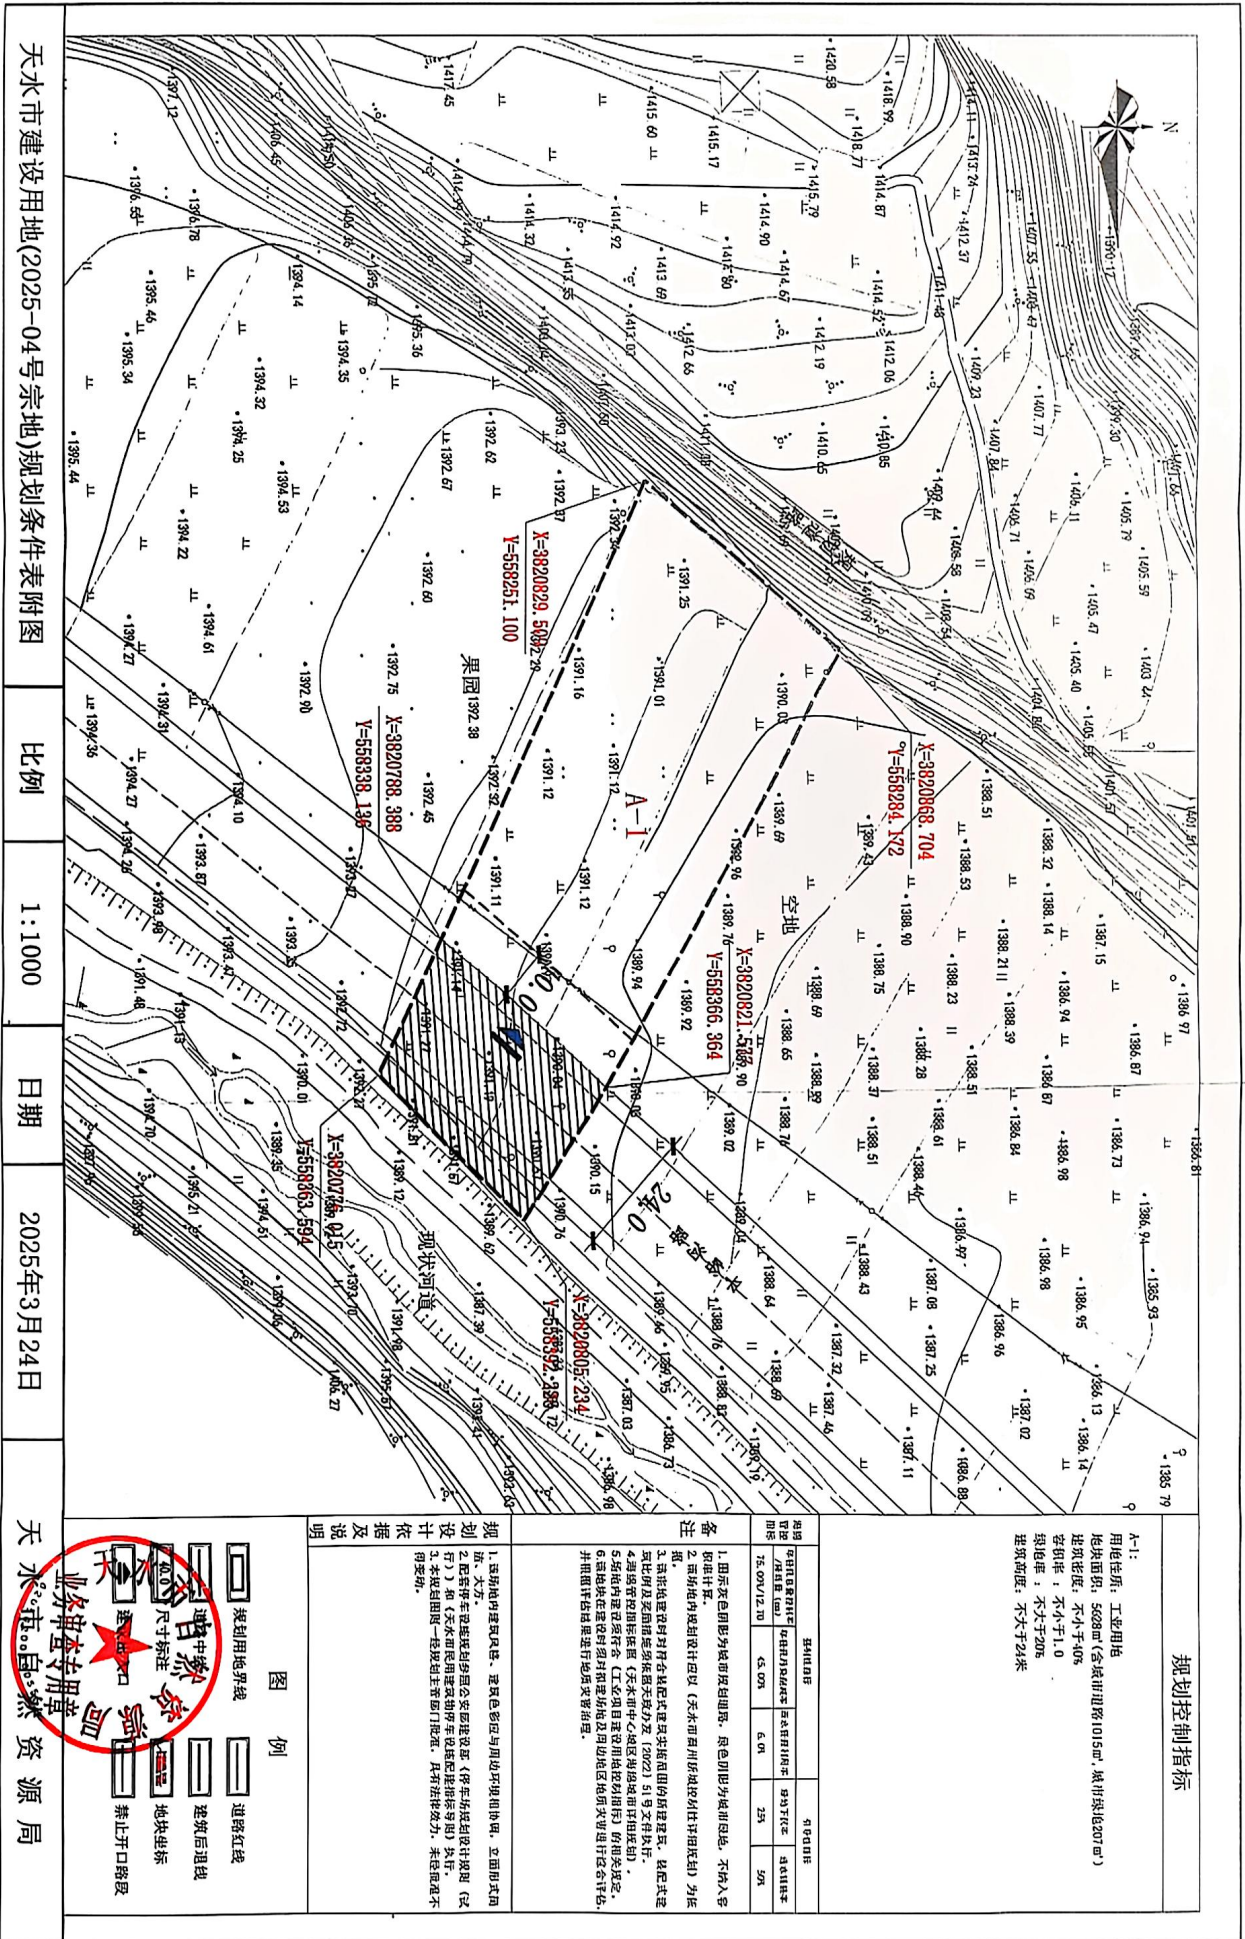

2025-3号挂牌宗地图

挂牌宗地图

单位: m

预编宗地代码: 6208021012200900312



天水市秦州区太京镇南苑村

天水市秦州区太京镇南苑村

用地总面积: 5628m²
 用地净面积: 4403m²
 规划道路面积: 1015m²
 城市绿地面积: 210m²

天水市秦州区太京镇南苑村

J1	0.06
J2	8.07
J3	10.08
J4	16.28
J5	14.41
J6	9.42
J7	5.53
J8	8.53
J9	2.22
J10	2.19
J11	0.32



测图单位: 天水市自然资源局规划研究院有限公司
 测图方法: 数字化成图
 测图时间: 2025年4月
 此图仅供挂牌时使用

1:1000



扫描全能王 创建



天水市自然资源局 建设用地规划条件表

编号：2025-04

建设用地位置	天水市秦州区太京镇席范村片区						
建设用地范围	东至现状河道，西至规划道路，南至果园，北至现状杨师傅清真糕点房						
建设用地现状	空地						
规划用地性质	工业用地						
建设用地面积	11228 m ² （含城市道路 1015 m ² ，城市绿地 207 m ² ）						
规划控制指标	容积率	不小于 1.0					
	建筑密度	不小于 40%					
	绿地率	不大于 20%					
	建筑高度	不大于 24 米					
建设用地规划条件	海绵管控指标	强制性指标			引导性指标		
		年径流总量控制率/降雨量（mm）	年径流污染削减率	雨水资源利用率	绿地下沉率	透水铺装率	
		75.00%/12.70	45.00%	6.0%	25%	50%	
		1. 图示灰色阴影为城市规划道路，绿色阴影为城市绿地，不纳入容积率计算。 2. 该场地内规划设计应以《天水市秦州新城控制性详细规划》为依据。 3. 该宗地建设时须符合装配式建筑实施范围内的新建建筑，装配式建筑比例及美面措施须依据天政办发〔2022〕51号文件执行。 4. 海绵管控指标依据《天水市中心城区海绵城市详细规划》。 5. 场地内建设须符合《工业项目建设用地控制指标》的相关规定。 6. 该地块在建设时须对拟建场地及周边地区地质灾害进行评估，并根据评估结果进行地质灾害治理。					
备注							
附件	2025-04 号建设用地规划条件表附图						
备注	1. 附件与本表具有同等效力。 2. 建设单位须严格按照规划条件进行设计。 3. 建设单位在取得土地使用权前应认真测算，在取得土地使用权后不得擅自更改。 4. 该规划条件有效期限为一年，在一年内不进行建设活动，该条件自动失效。						

2025年3月25日